
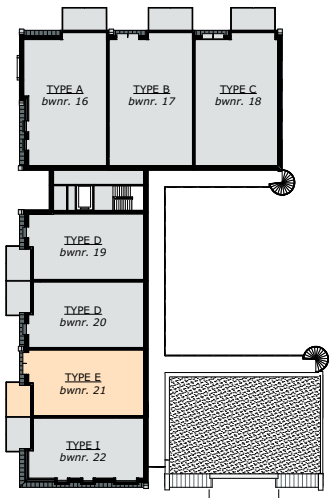


RENVOOI

Posities aansluitpunten zijn indicatief, genoemde maten kunnen wijzigen t.g.v. verdere uitwerking

- lichtpunt met aanduiding t.b.v. schakelaar
- rookmelder
- wandlichtpunt met aanduiding t.b.v. schakelaar (2.000+ vl.)
- enkel polige schakelaar met aanduiding t.b.v. lichtpunt
- wisselschakelaar met aanduiding t.b.v. lichtpunt
- serieschakelaar met aanduiding t.b.v. lichtpunt
- schakelaar ventilatie badkamer
- enkele wandcontactdoos geaard (300+ vl.)
- dubbele wandcontactdoos geaard (300+ vl.)
- enkele wandcontactdoos geaard t.b.v. koelkast (50+ vl.)
- enkele wandcontactdoos geaard t.b.v. afzuigkap (2.350+ vl.)
- dubbele wandcontactdoos geaard t.b.v. huishoud (1.100+ vl.)
- perilex wandcontactdoos (2 fase) t.b.v. kookplaat (50+ vl.)
- thermostaat bedraad
- aansluitpunt t.b.v. data bedraad
- Co2 meter
- leiding onbedraad t.b.v. wasdroger (1.100+ vl.)
- leiding onbedraad t.b.v. vaatwasser (50+ vl.)
- beldrukker
- videofoon
- meterkast
- verdeler vloerverwarming
- vloerverwarming
- elektrische radiator badkamer
- circa maat (gemeten op 1,5 m')
- opstelplaats wasmachine/droger
- opstelplaats wtw unit
- opstelplaats warmtepomp

03A5.01
vensterbank Bianco C.

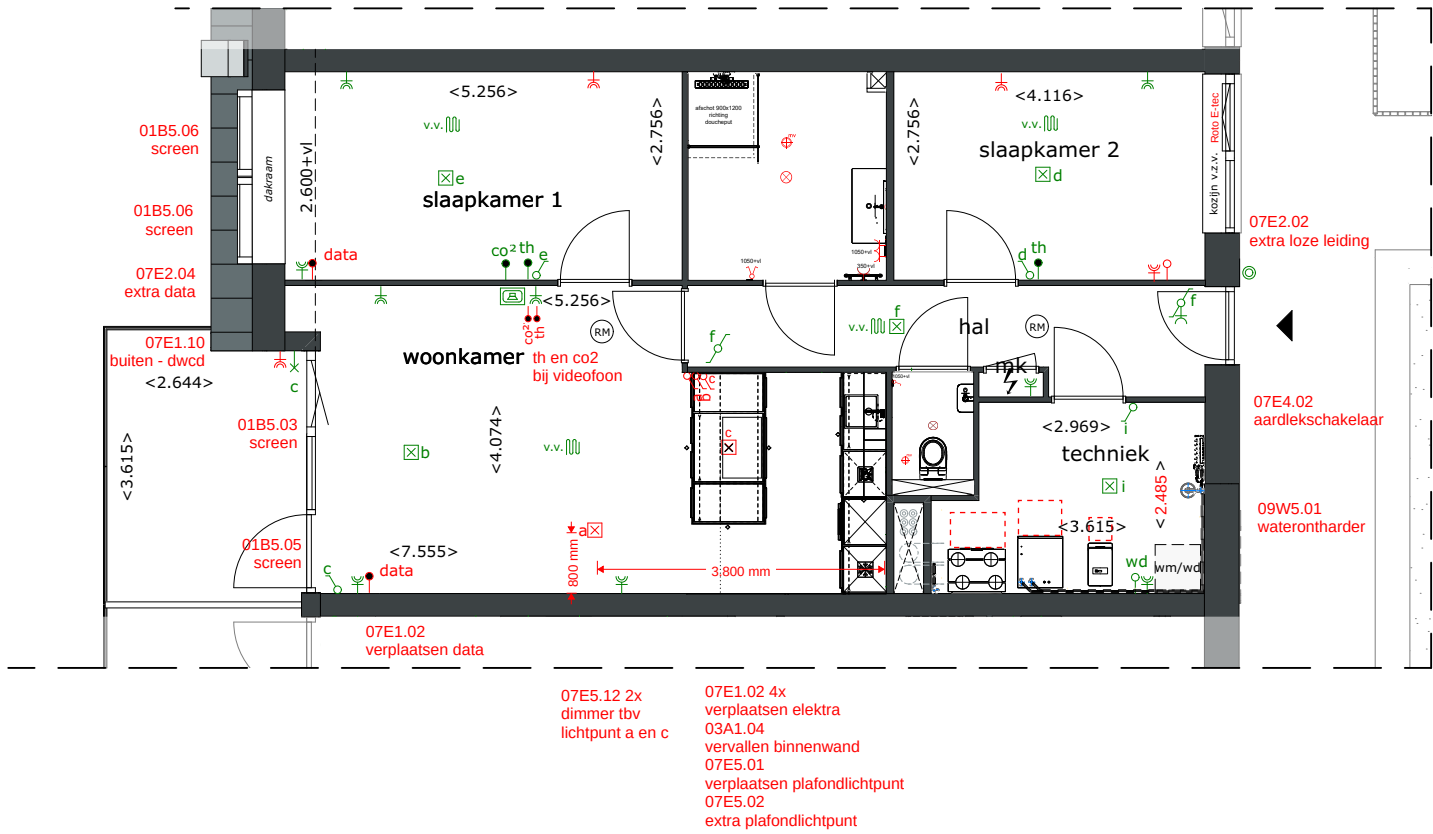

- Keuken volgens offerte Superkeukens
- Badkamer en toiletruimte volgens offerte Plieger en Lingenkeramiek.
- Binnendeuren volgens offerte Berkvens.

2E VERDIEPING BOUWNUMMER 21